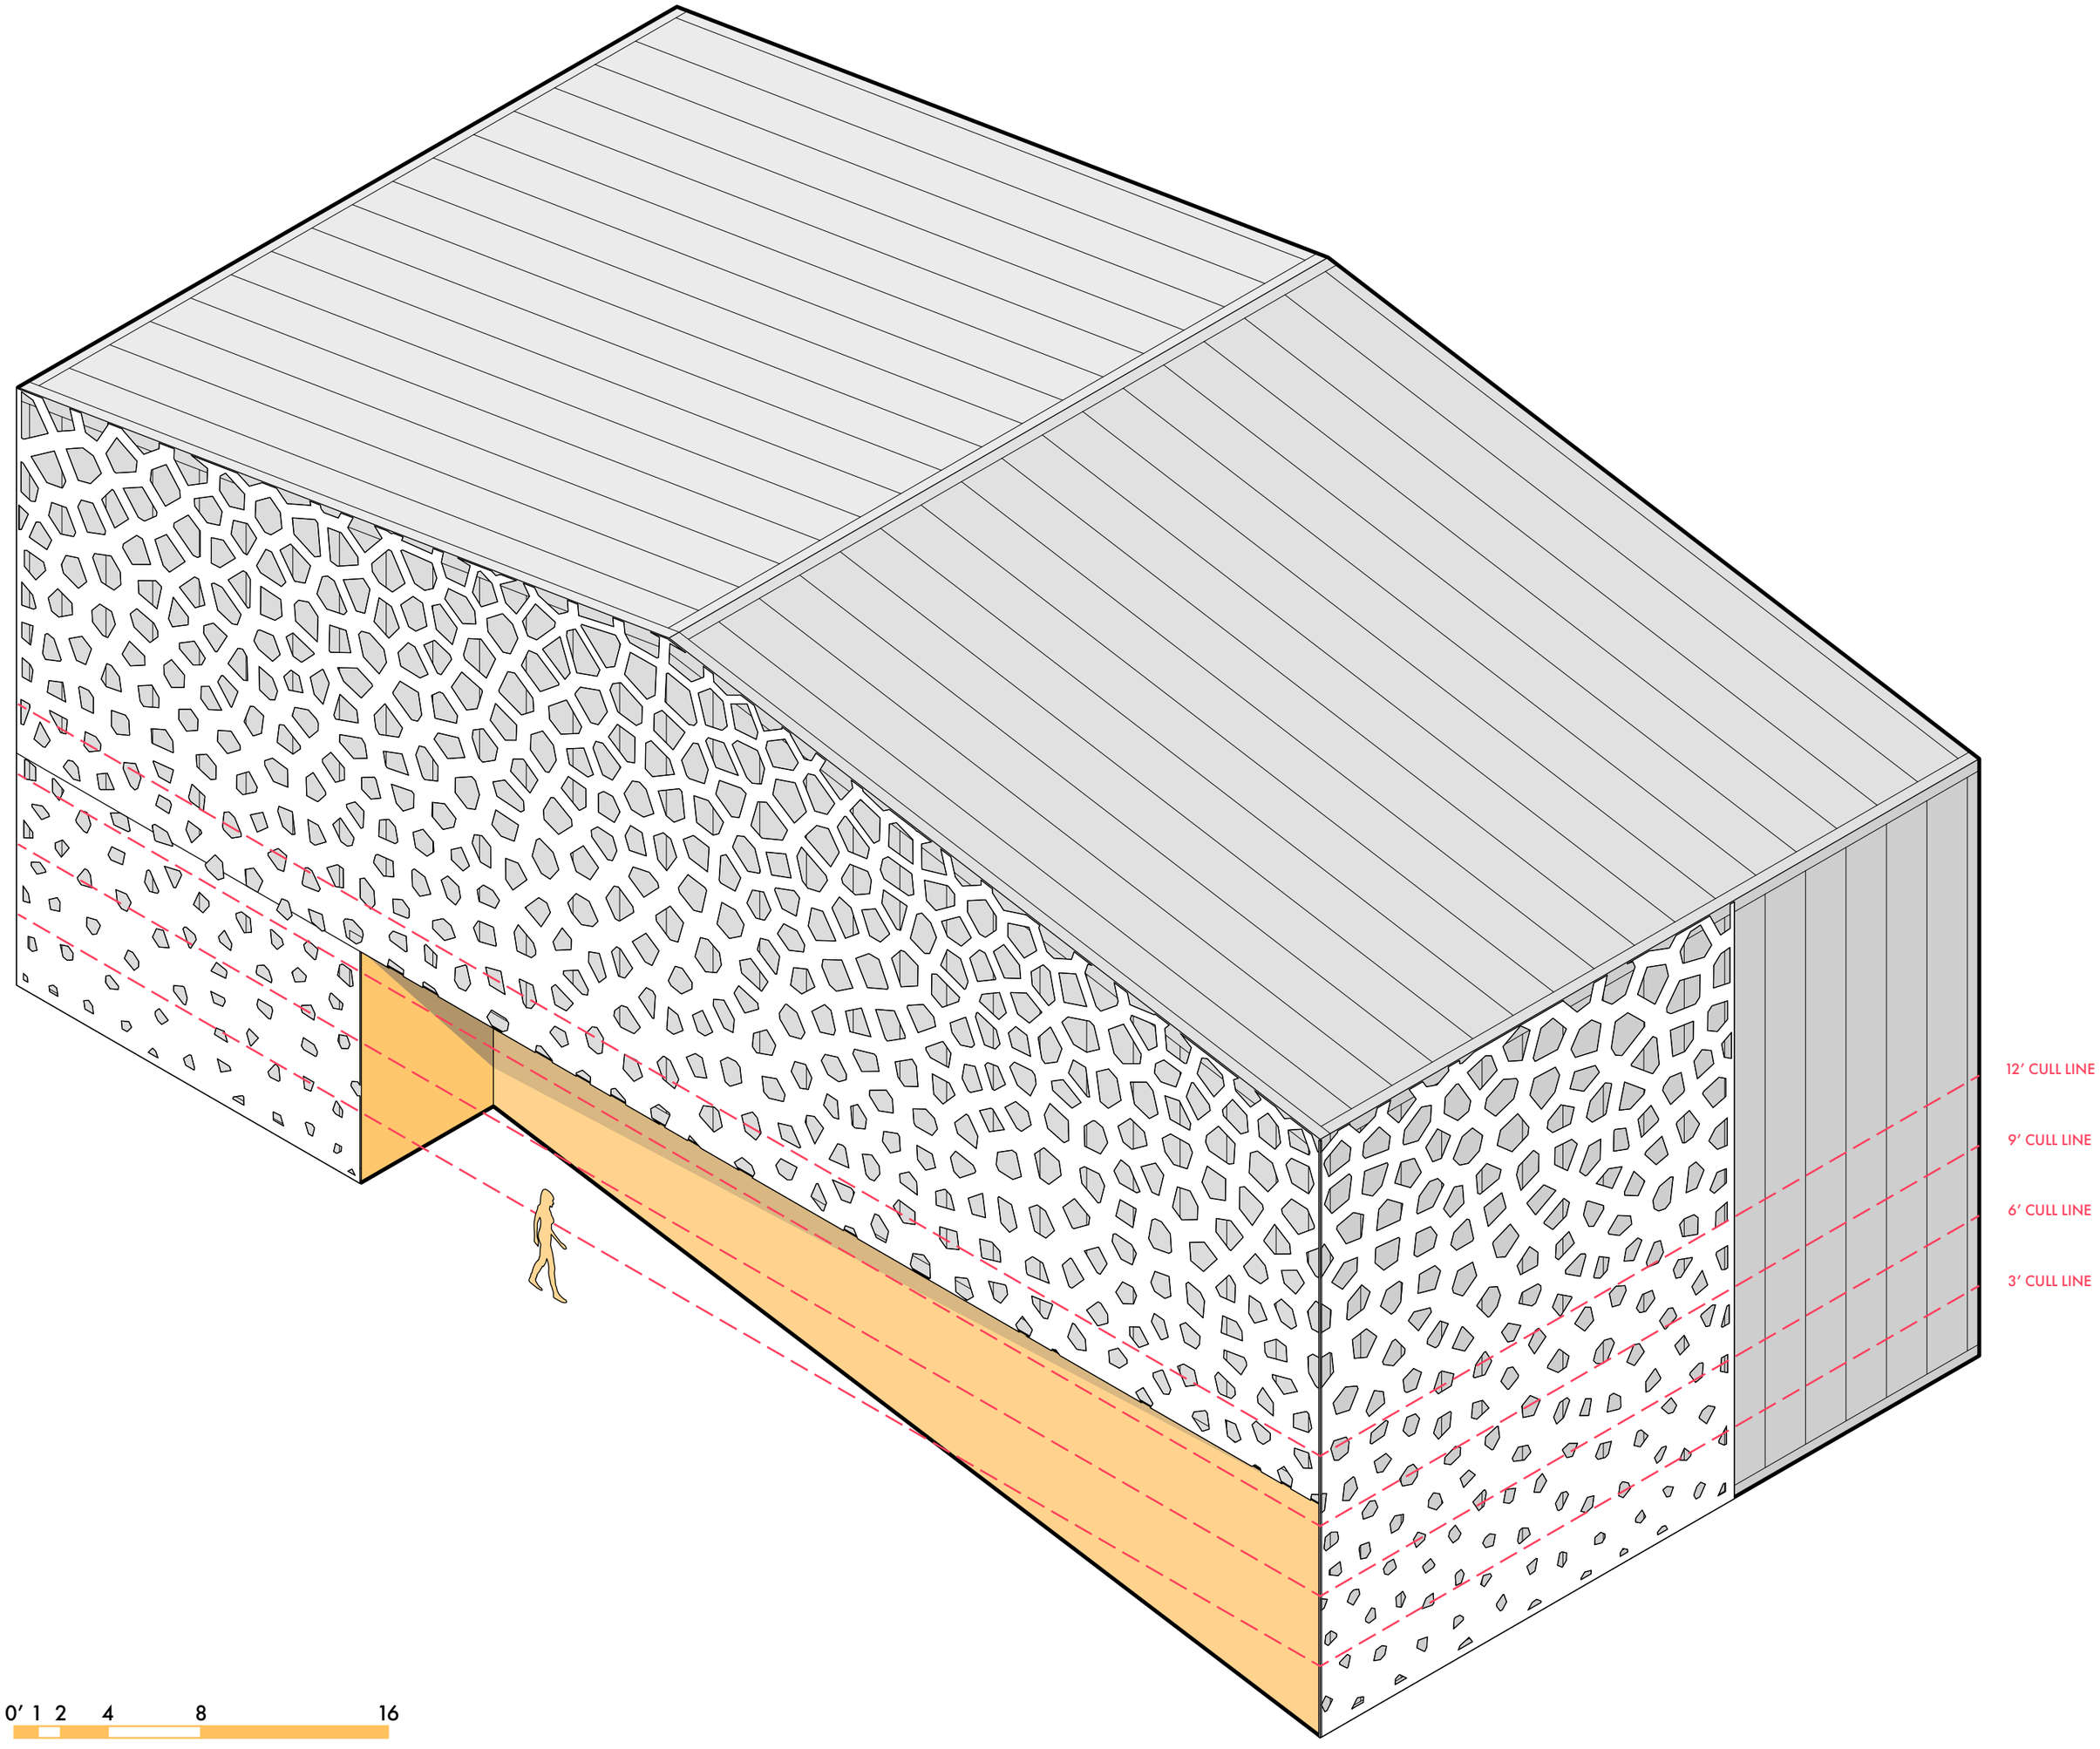
12′ CULL LINE
9′ CULL LINE
6′ CULL LINE
3′ CULL LINE
0′ 1 2 4 8 16

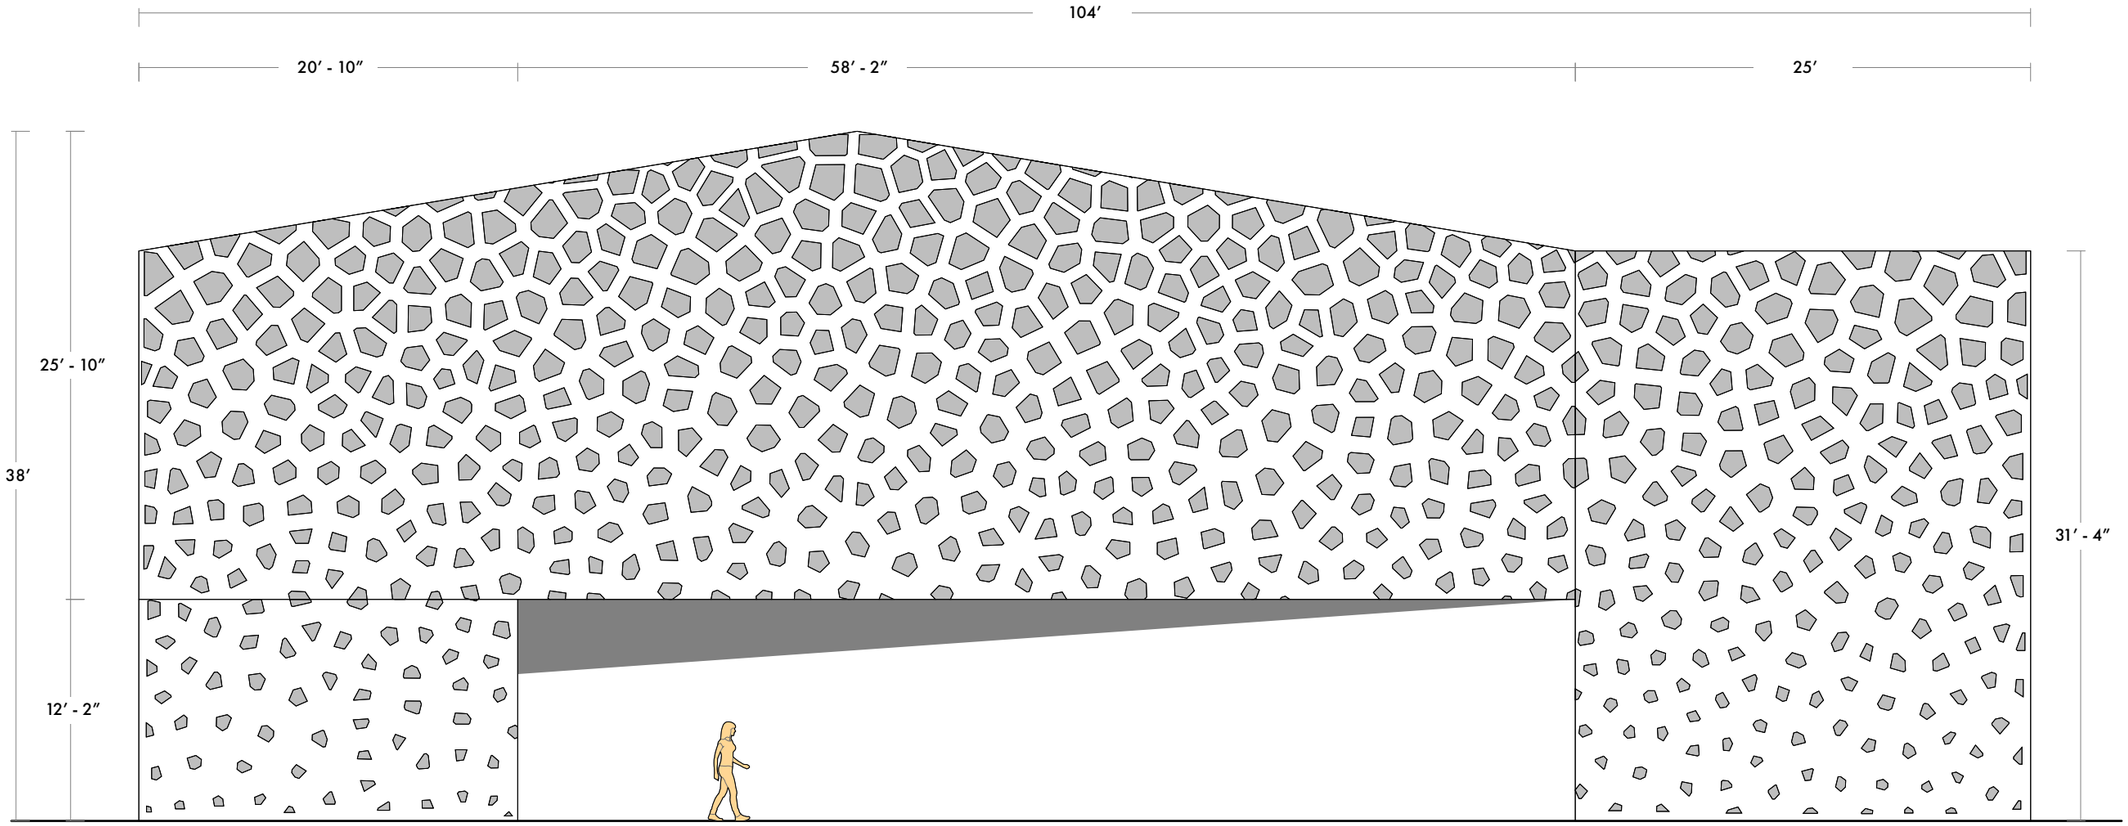

UNROLLED ELEVATION

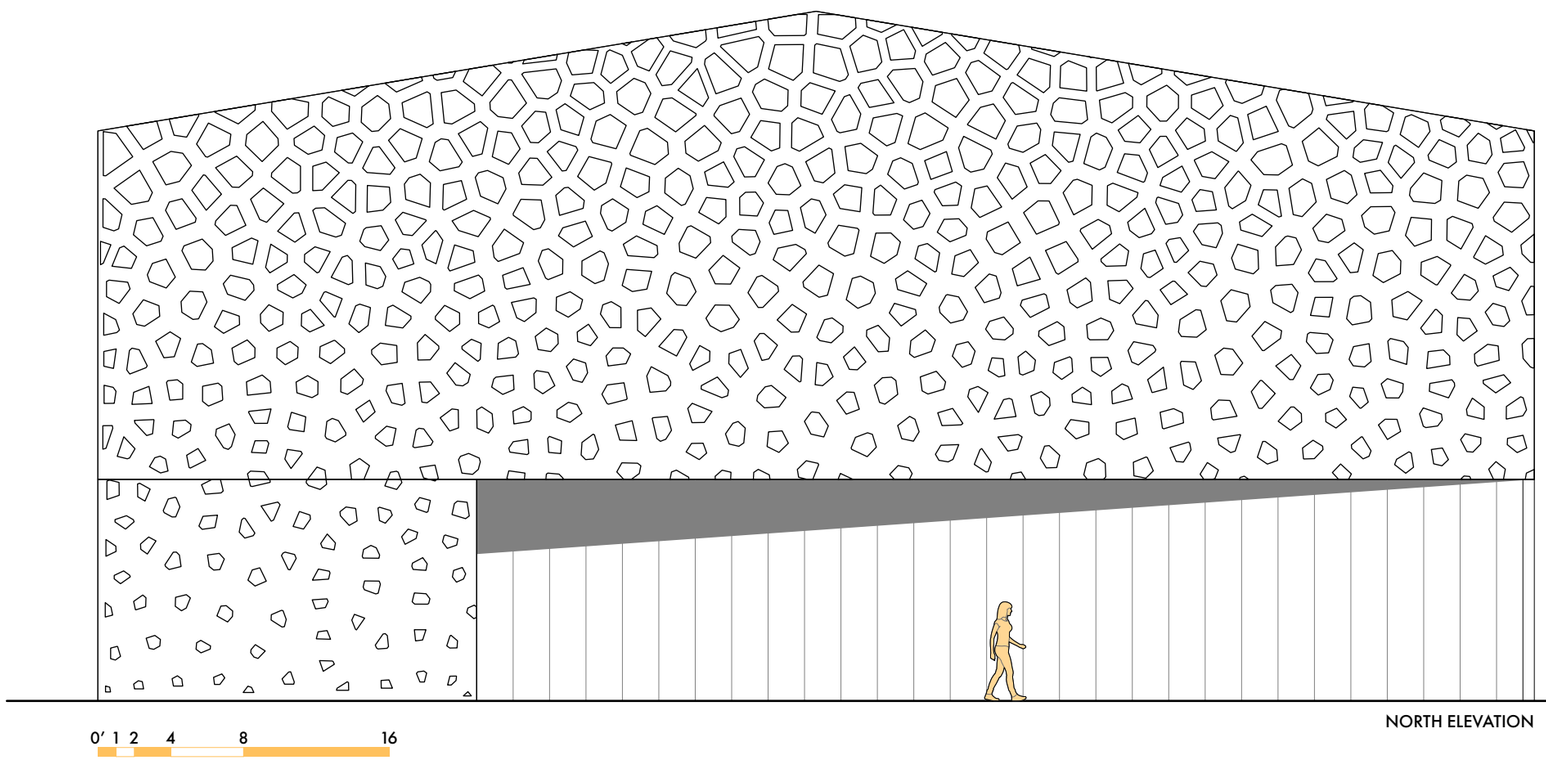

NORTH ELEVATION

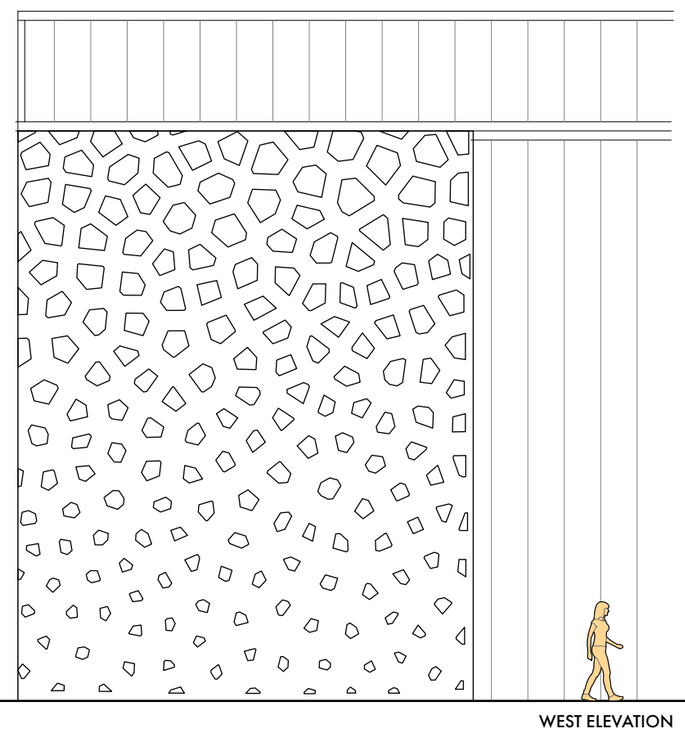

WEST ELEVATION

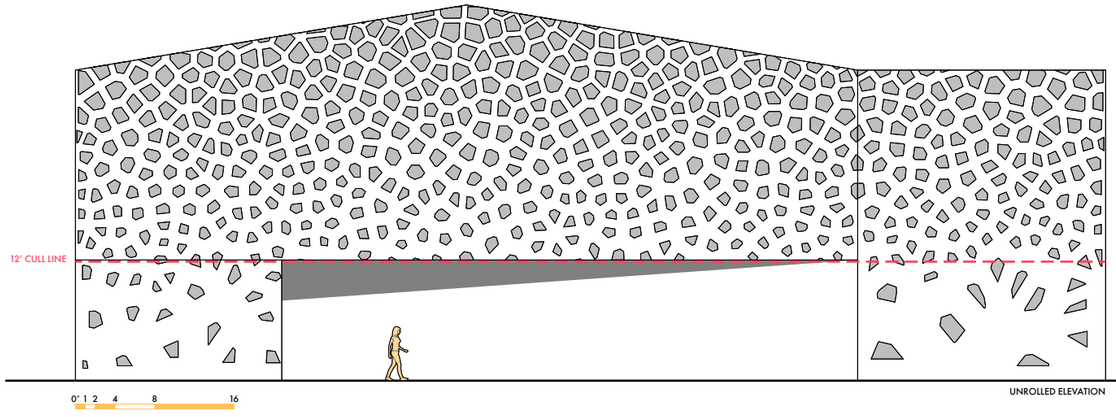

UNROLLED ELEVATION

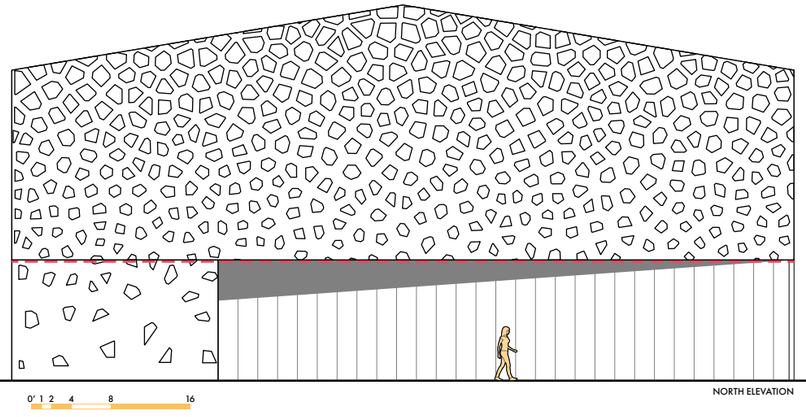

NORTH ELEVATION

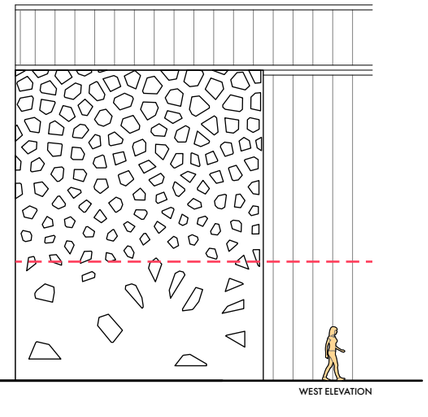

WEST ELEVATION

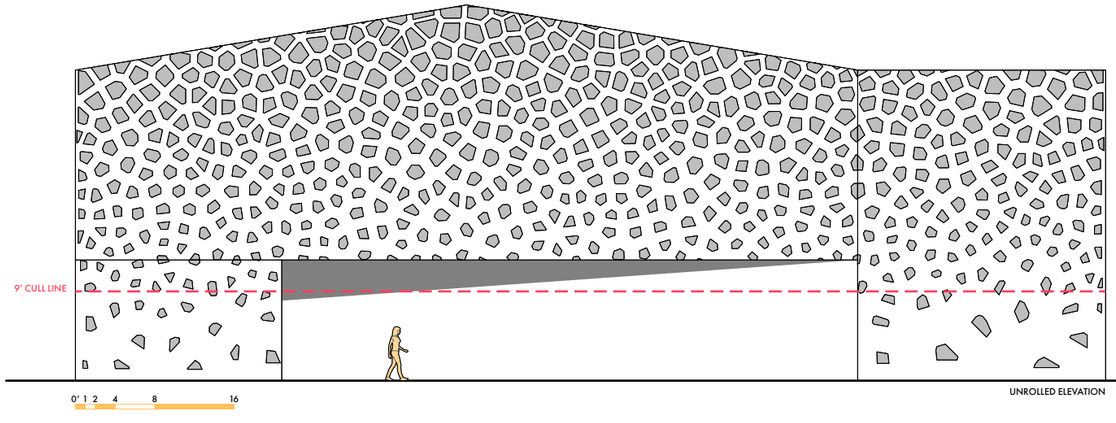

UNROLLED ELEVATION

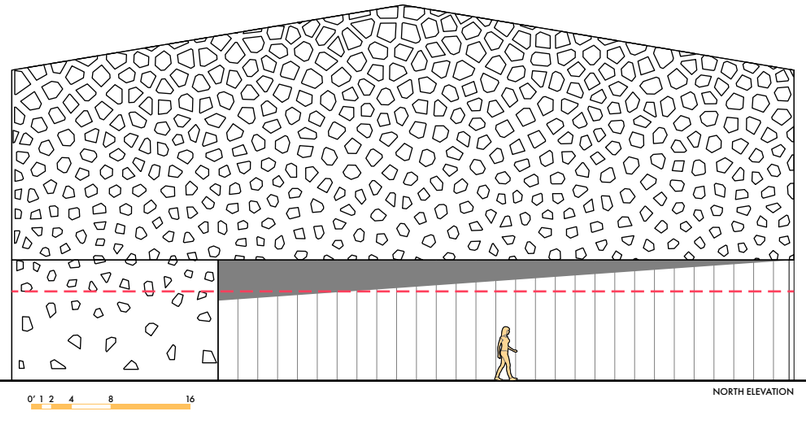

NORTH ELEVATION

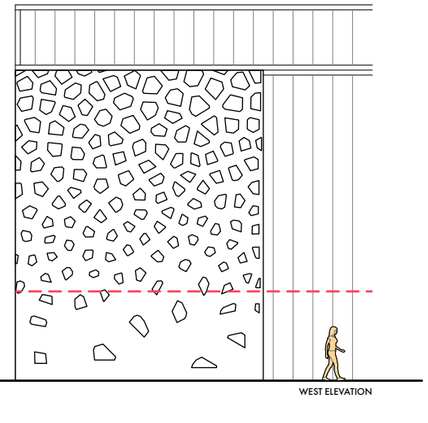

WEST ELEVATION

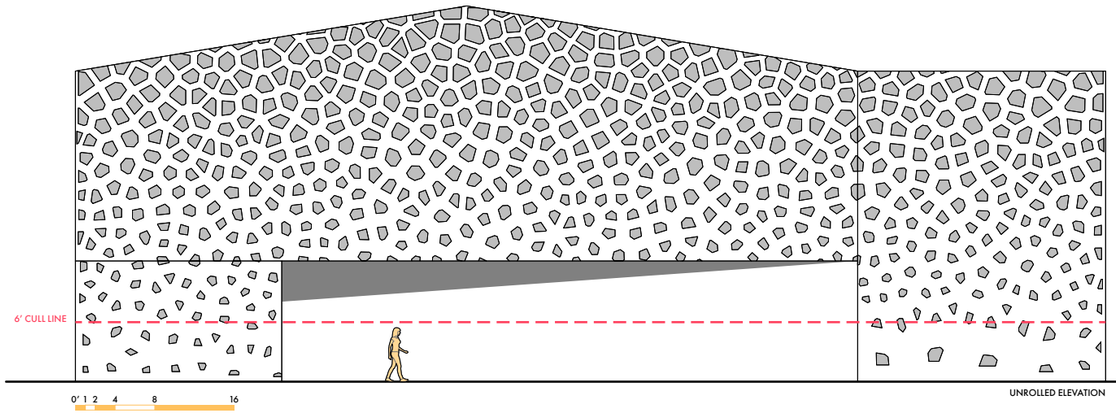

UNROLLED ELEVATION

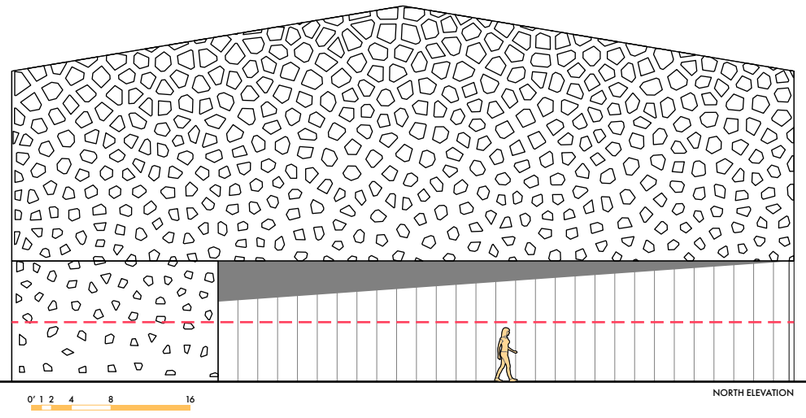

NORTH ELEVATION

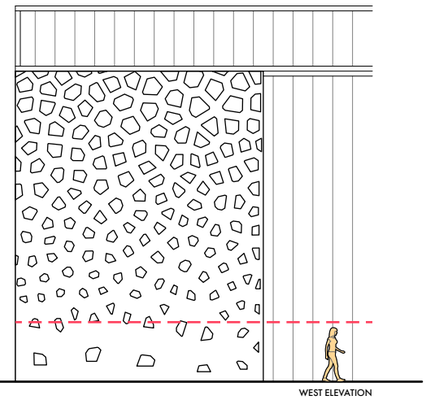

WEST ELEVATION

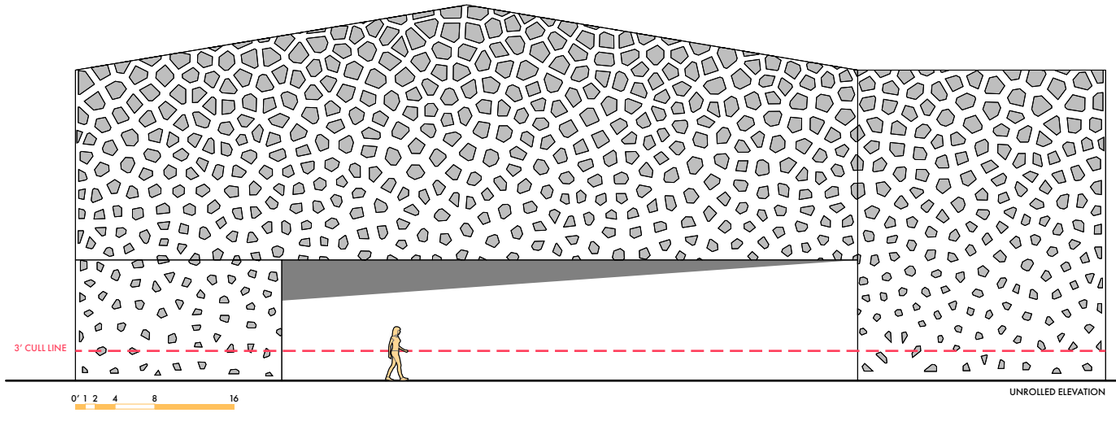

UNROLLED ELEVATION

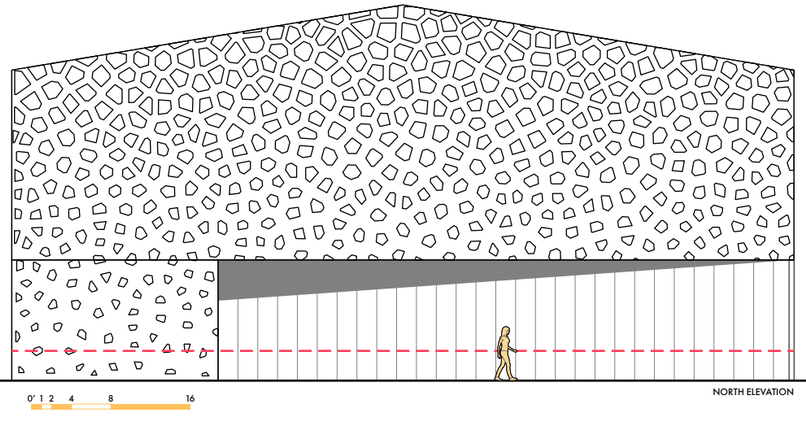

NORTH ELEVATION

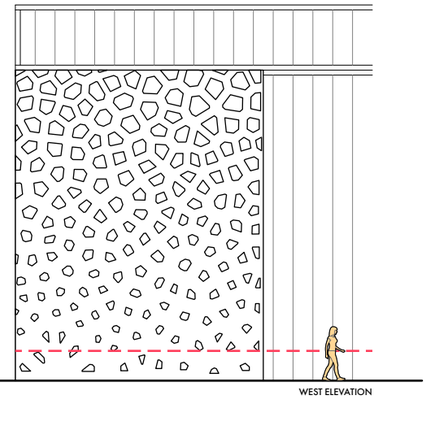

WEST ELEVATION